




US Army Corps of Engineers ®

GRISSOM AIR RESERVE BASE
 INDOOR SMALL ARMS RANGE
 P2 502689, FY 25
 PN CTGB12-9032

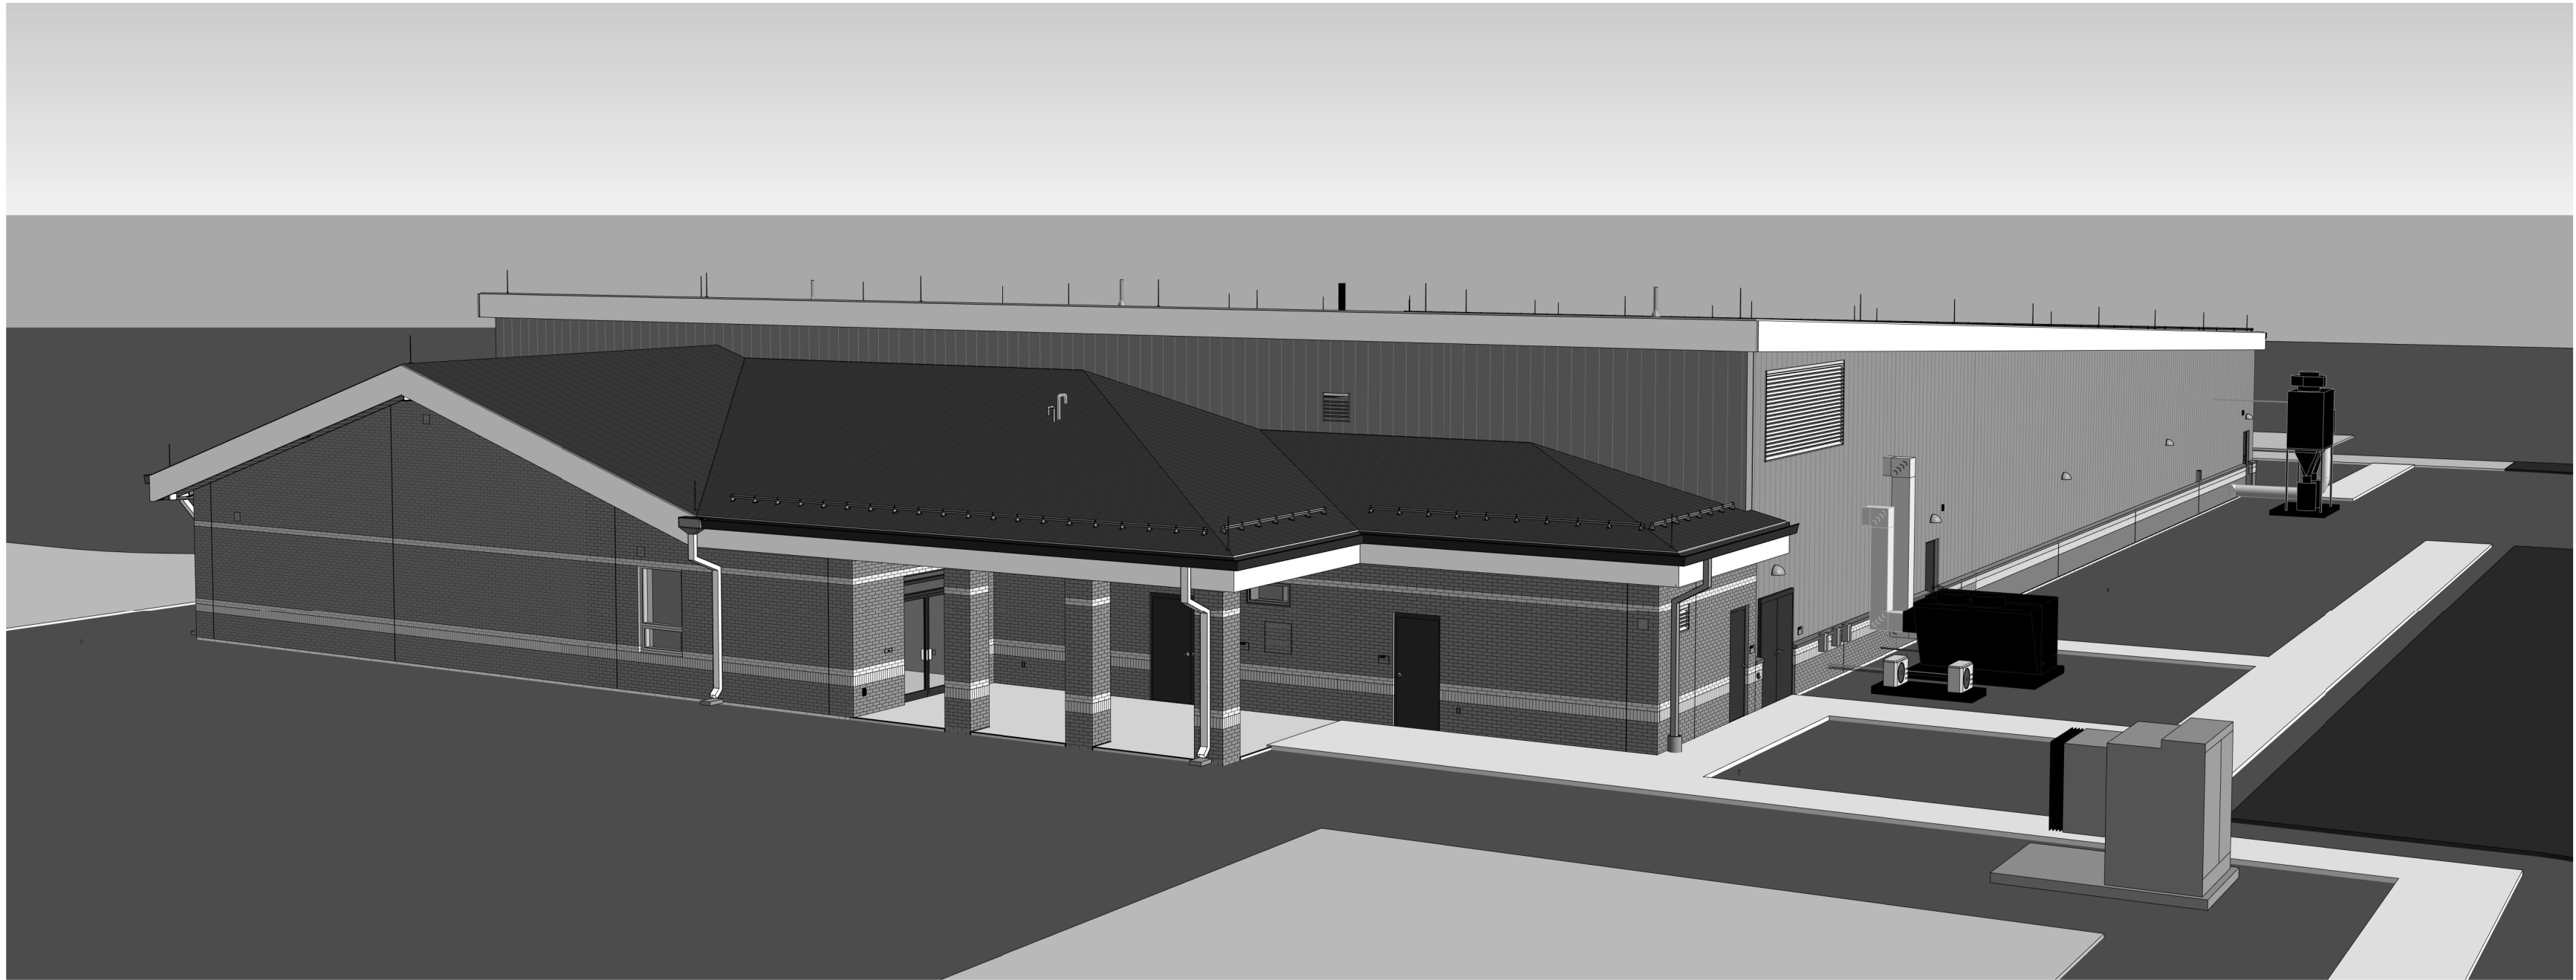

SOLICITATION NO.:
CONTRACT NO.:
ISSUE DATE: SEP 2024
VOLUME:

12 December 2024
W912QR25B0001

SIGNATURES BELOW INCLUDE DESIGNERS AND CHECKERS ON ALL SHEETS INCLUDED IN THE FOLLOWING DRAWING SET.	
FIRE ALARM	LIFE SAFETY
DESIGNER: C. KRISH	CIVIL ITR: B. DORSCH
CHECKER: B. GADDIE	ARCH ITR: C. MUDD
PLUMBING	MECH ITR: C. GREENWELL
DESIGNER: H.A. LE	ELEC ITR: J. MOORE
CHECKER: V. NGUYEN	GEOTECHNICAL
MECHANICAL	DESIGNER: D. DONNELLY
DESIGNER: H.A. LE	CHECKER: E. SPRINGSTON
CHECKER: V. NGUYEN	HYDROLOGY
ELECTRICAL	DESIGNER: C. CARTER
DESIGNER: C. KRISH	CHECKER: I. WEILBAKER
CHECKER: B. GADDIE	CIVIL
TELECOMMUNICATIONS	DESIGNER: C. CARTER
DESIGNER: C. KRISH	CHECKER: T. SMITH
CHECKER: B. GADDIE	STRUCTURAL
FIRE PROTECTION	DESIGNER: A. DALEY
DESIGNER: V. NGUYEN	CHECKER: N. FITCH
CHECKER: C. GREENWELL	ARCHITECTURE
INTERIOR DESIGN	DESIGNER: J. MacMILLAN
DESIGNER: J. O'BRYAN	CHECKER: J. SCHENKENFELDER
CHECKER: C. MURPHY	

SIGNATURES AFFIXED BELOW INDICATE
OFFICIAL RECOMMENDATION AND
APPROVAL OF ALL DRAWINGS IN THIS SET.

APPROVAL RECOMMENDED: *

J. MACMILLAN
TECHNICAL LEAD

*APPROVAL RECOMMENDED SIGNATURE
INDICATES DESIGN AND QUALITY
CONTROL REVIEWS ARE COMPLETE,
INCLUDING ITR/ATR CERTIFICATION.

APPROVED: **

IAN F. MITCHELL, PE
CHIEF, ENGINEERING DIVISION

** THIS PROJECT WAS DESIGNED BY THE
 U.S. ARMY CORPS OF ENGINEERS,
 LOUISVILLE DISTRICT. INDIVIDUALS
 WHOSE SIGNATURES AND REGISTRATION
 DESIGNATIONS APPEAR ON THESE
 DOCUMENTS ARE OPERATING WITHIN
 THE SCOPE OF THEIR EMPLOYMENT.
 SIGNATURES ARE REQUIRED BY ER
 1110-1-8152.

[illegible]

US ARMY CORPS OF ENGINEERS LOUISVILLE DISTRICT 600 DR. MARTIN LUTHER KING JR. PLACE LOUISVILLE, KY 40202	DESIGNED BY: J. MACMILLAN	ISSUE DATE: SEPTEMBER 2024
	CHECKED BY: R. HOOL	SOLICITATION NO.:
	CHECKED BY: J. SCHENKENFELDER	CONTRACT NO.:
	SUBMITTED BY:	
	SIZE: ANSI D	

GRISSOM AIR RESERVE BASE
INDOOR SMALL ARMS RANGE
P/N CTGB129032, P2 502689, FY 25

COVER SHEET

SHEET ID


G-001


CERTIFIED FINAL


Plot Date: 9/5/2024 2:41:48 PM

W912QR25B0001 Plans-0000


CERTIFIED FINANCIAL

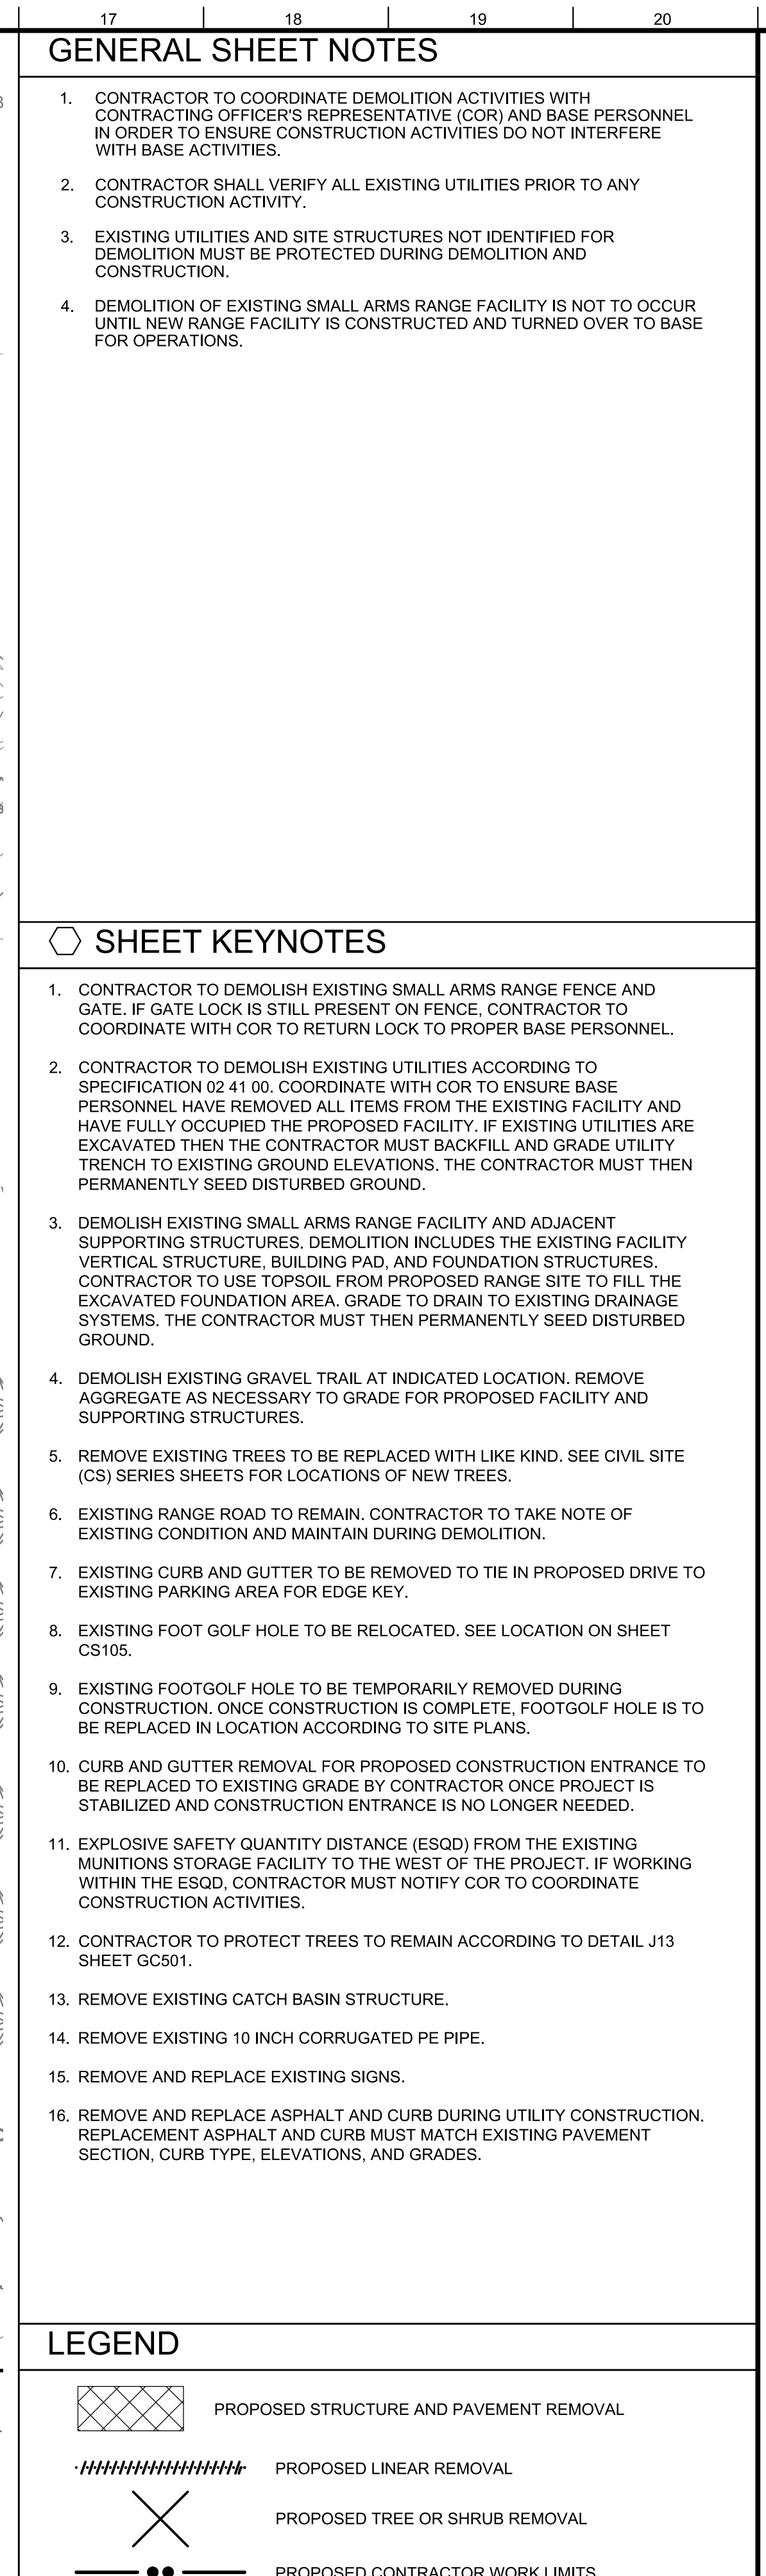


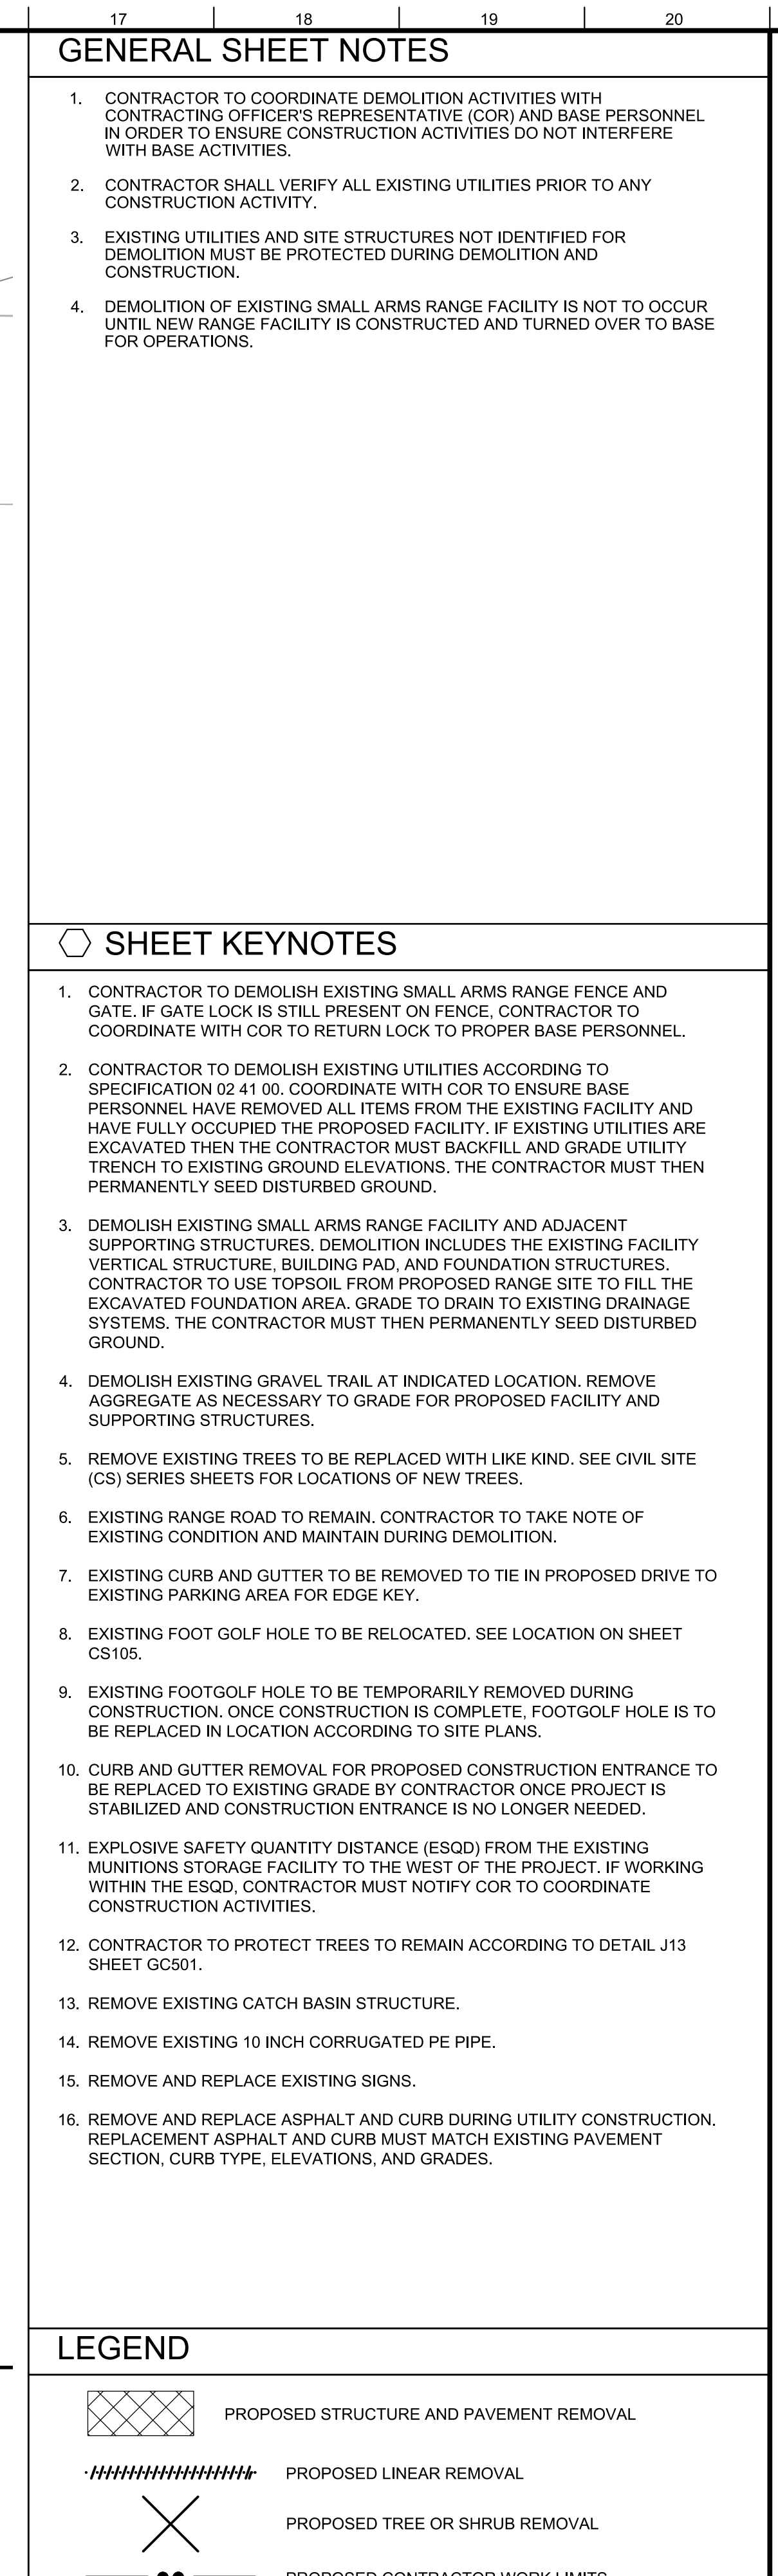


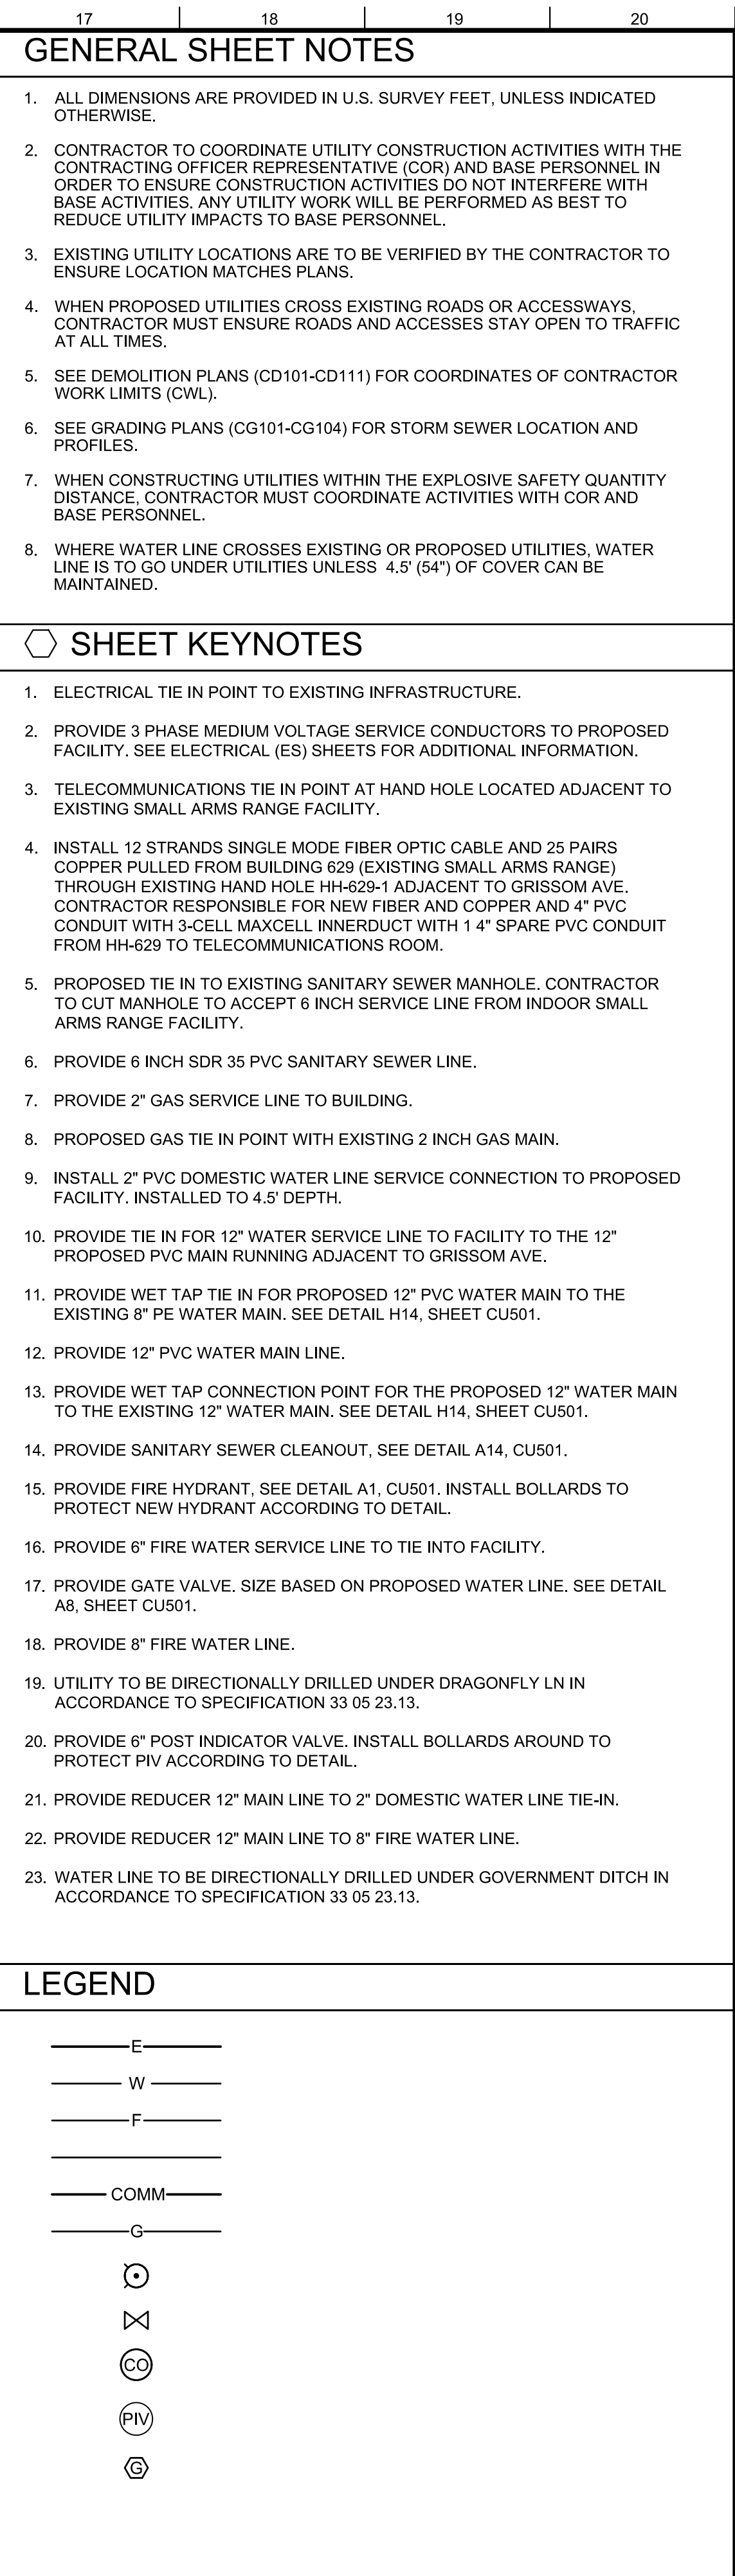


RTIFIED FINAL W912QR25B00001 Plans-0000

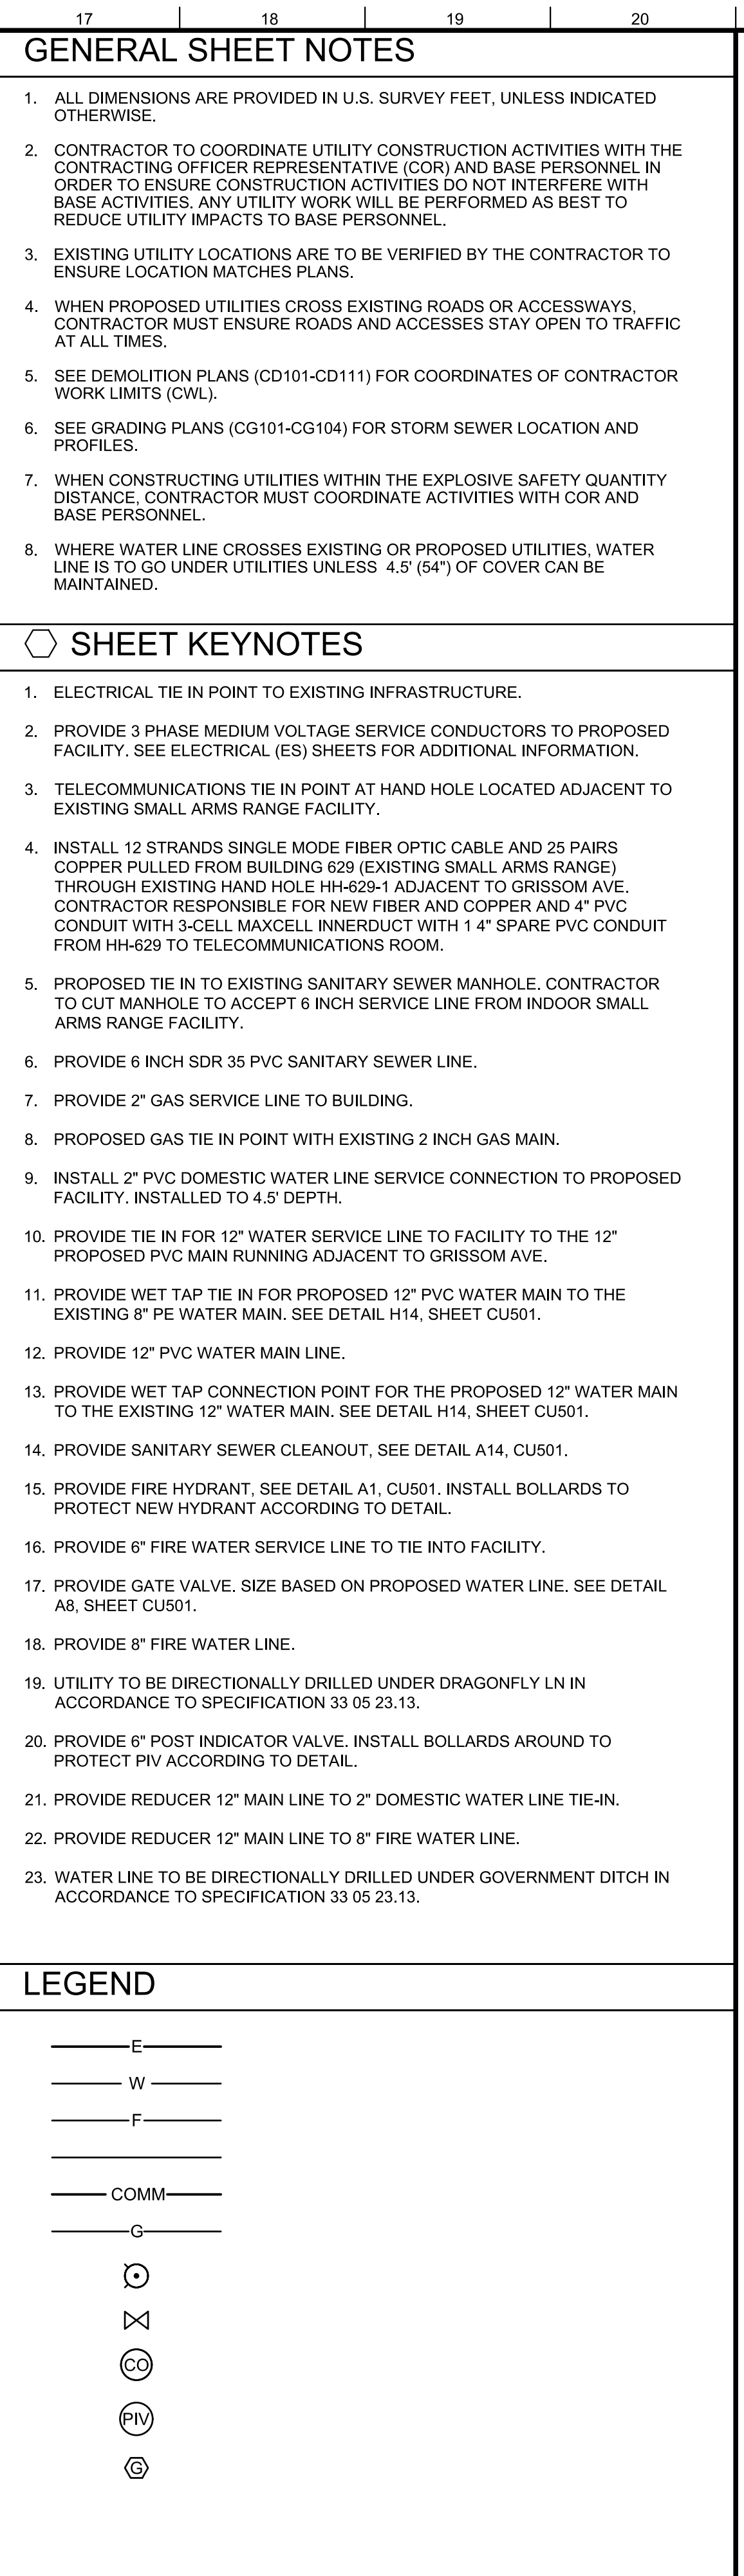

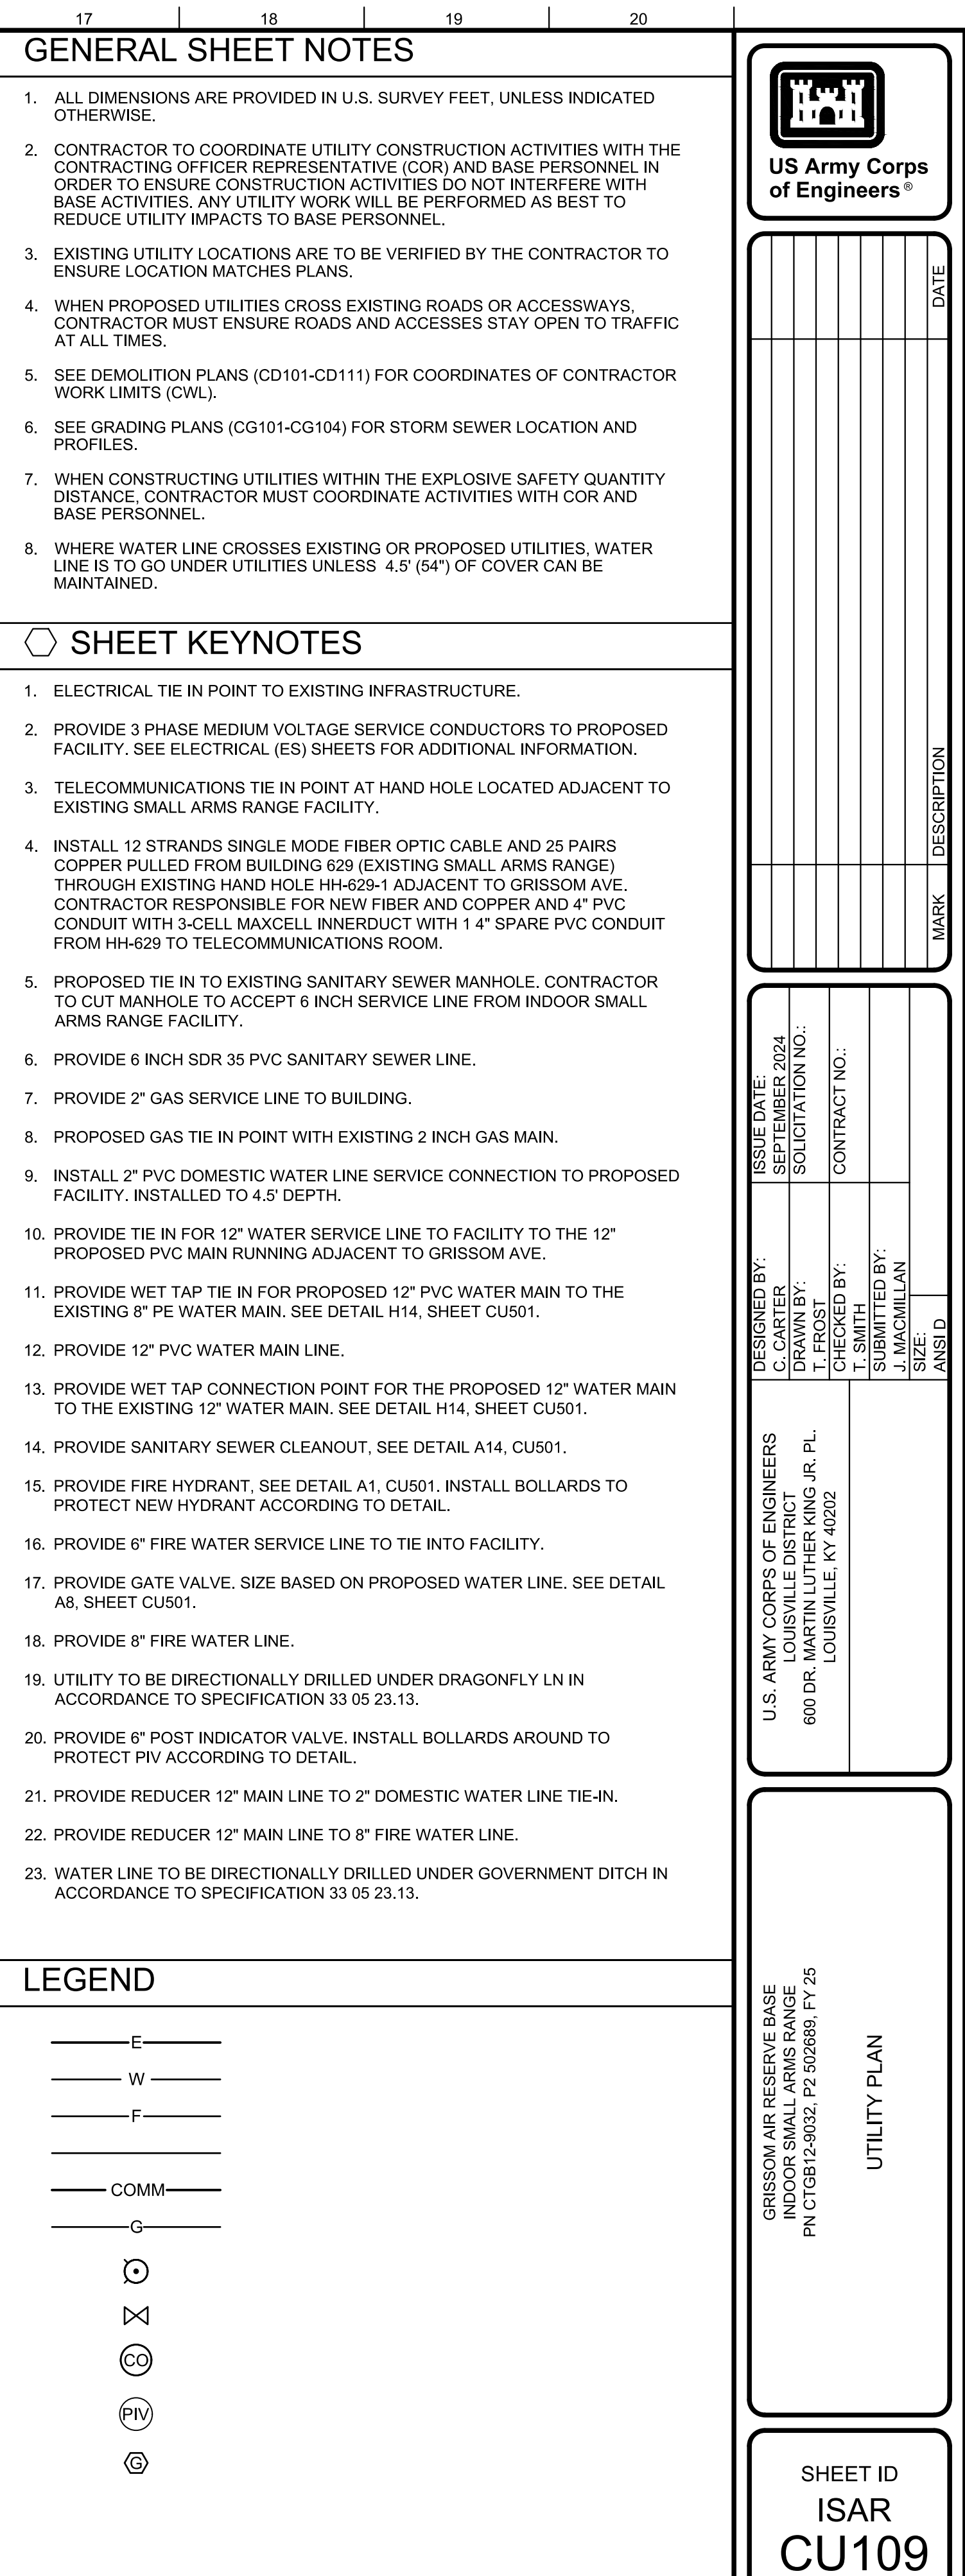


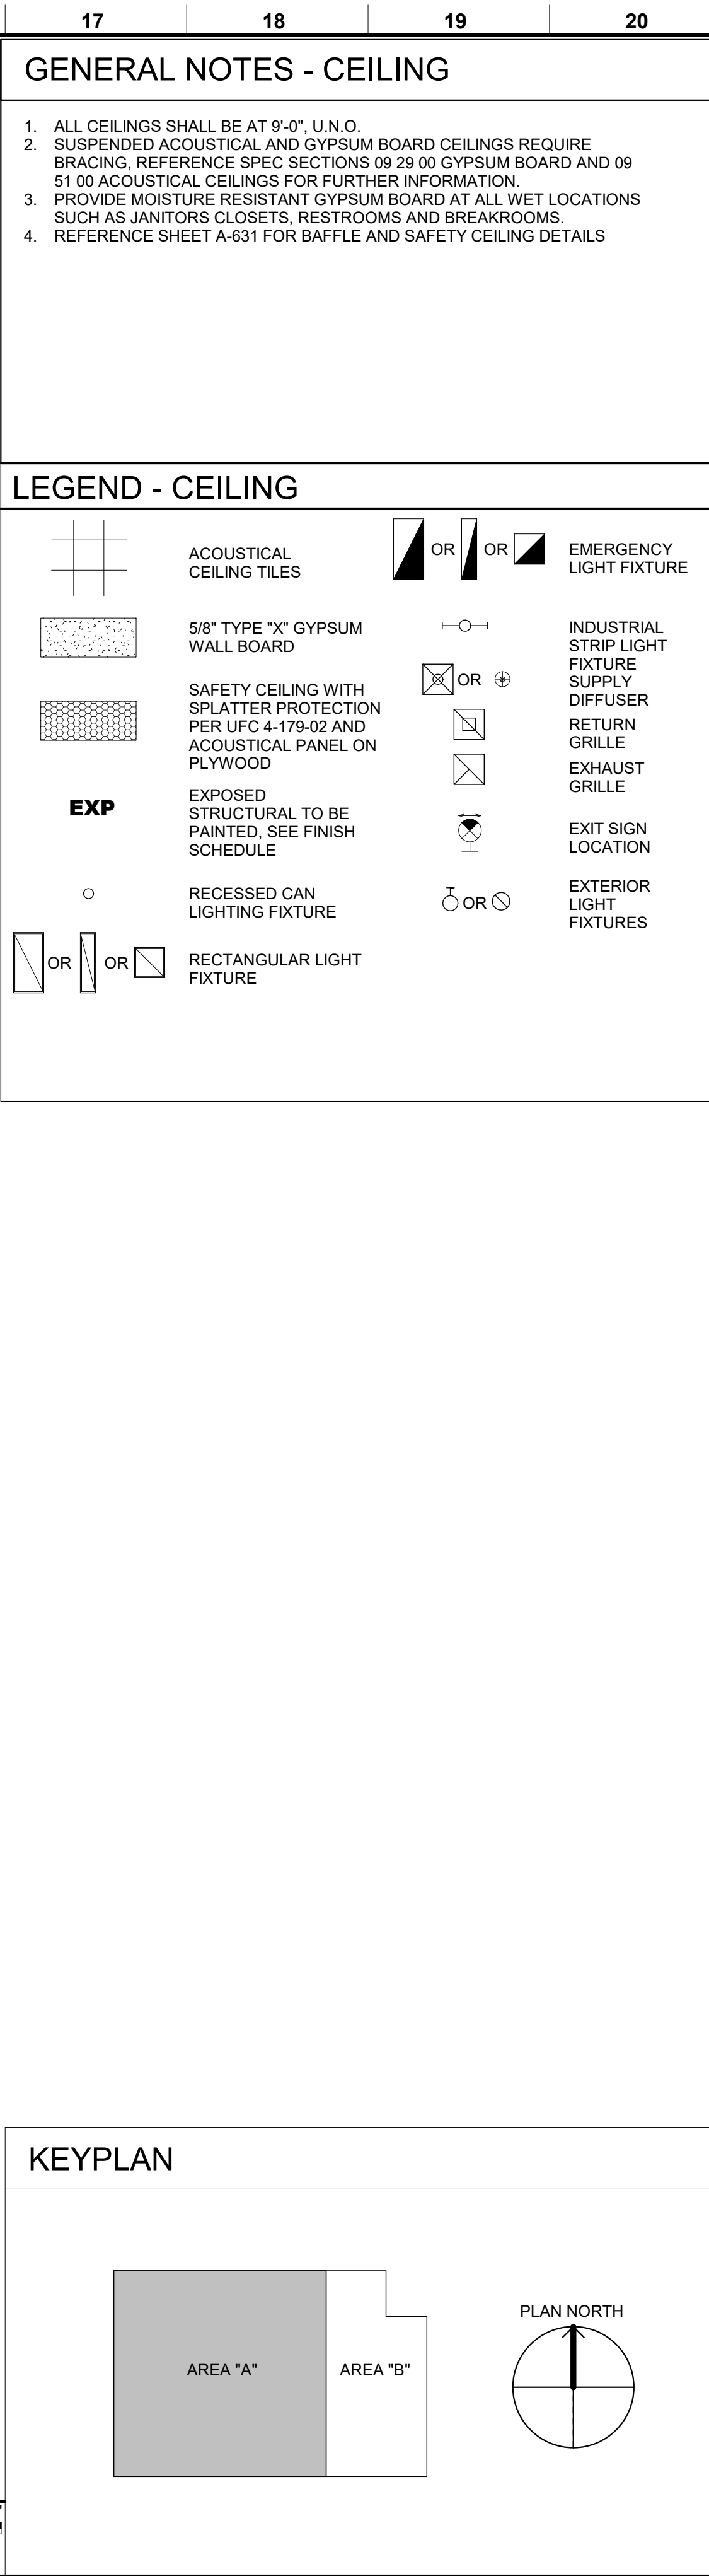
[illegible]

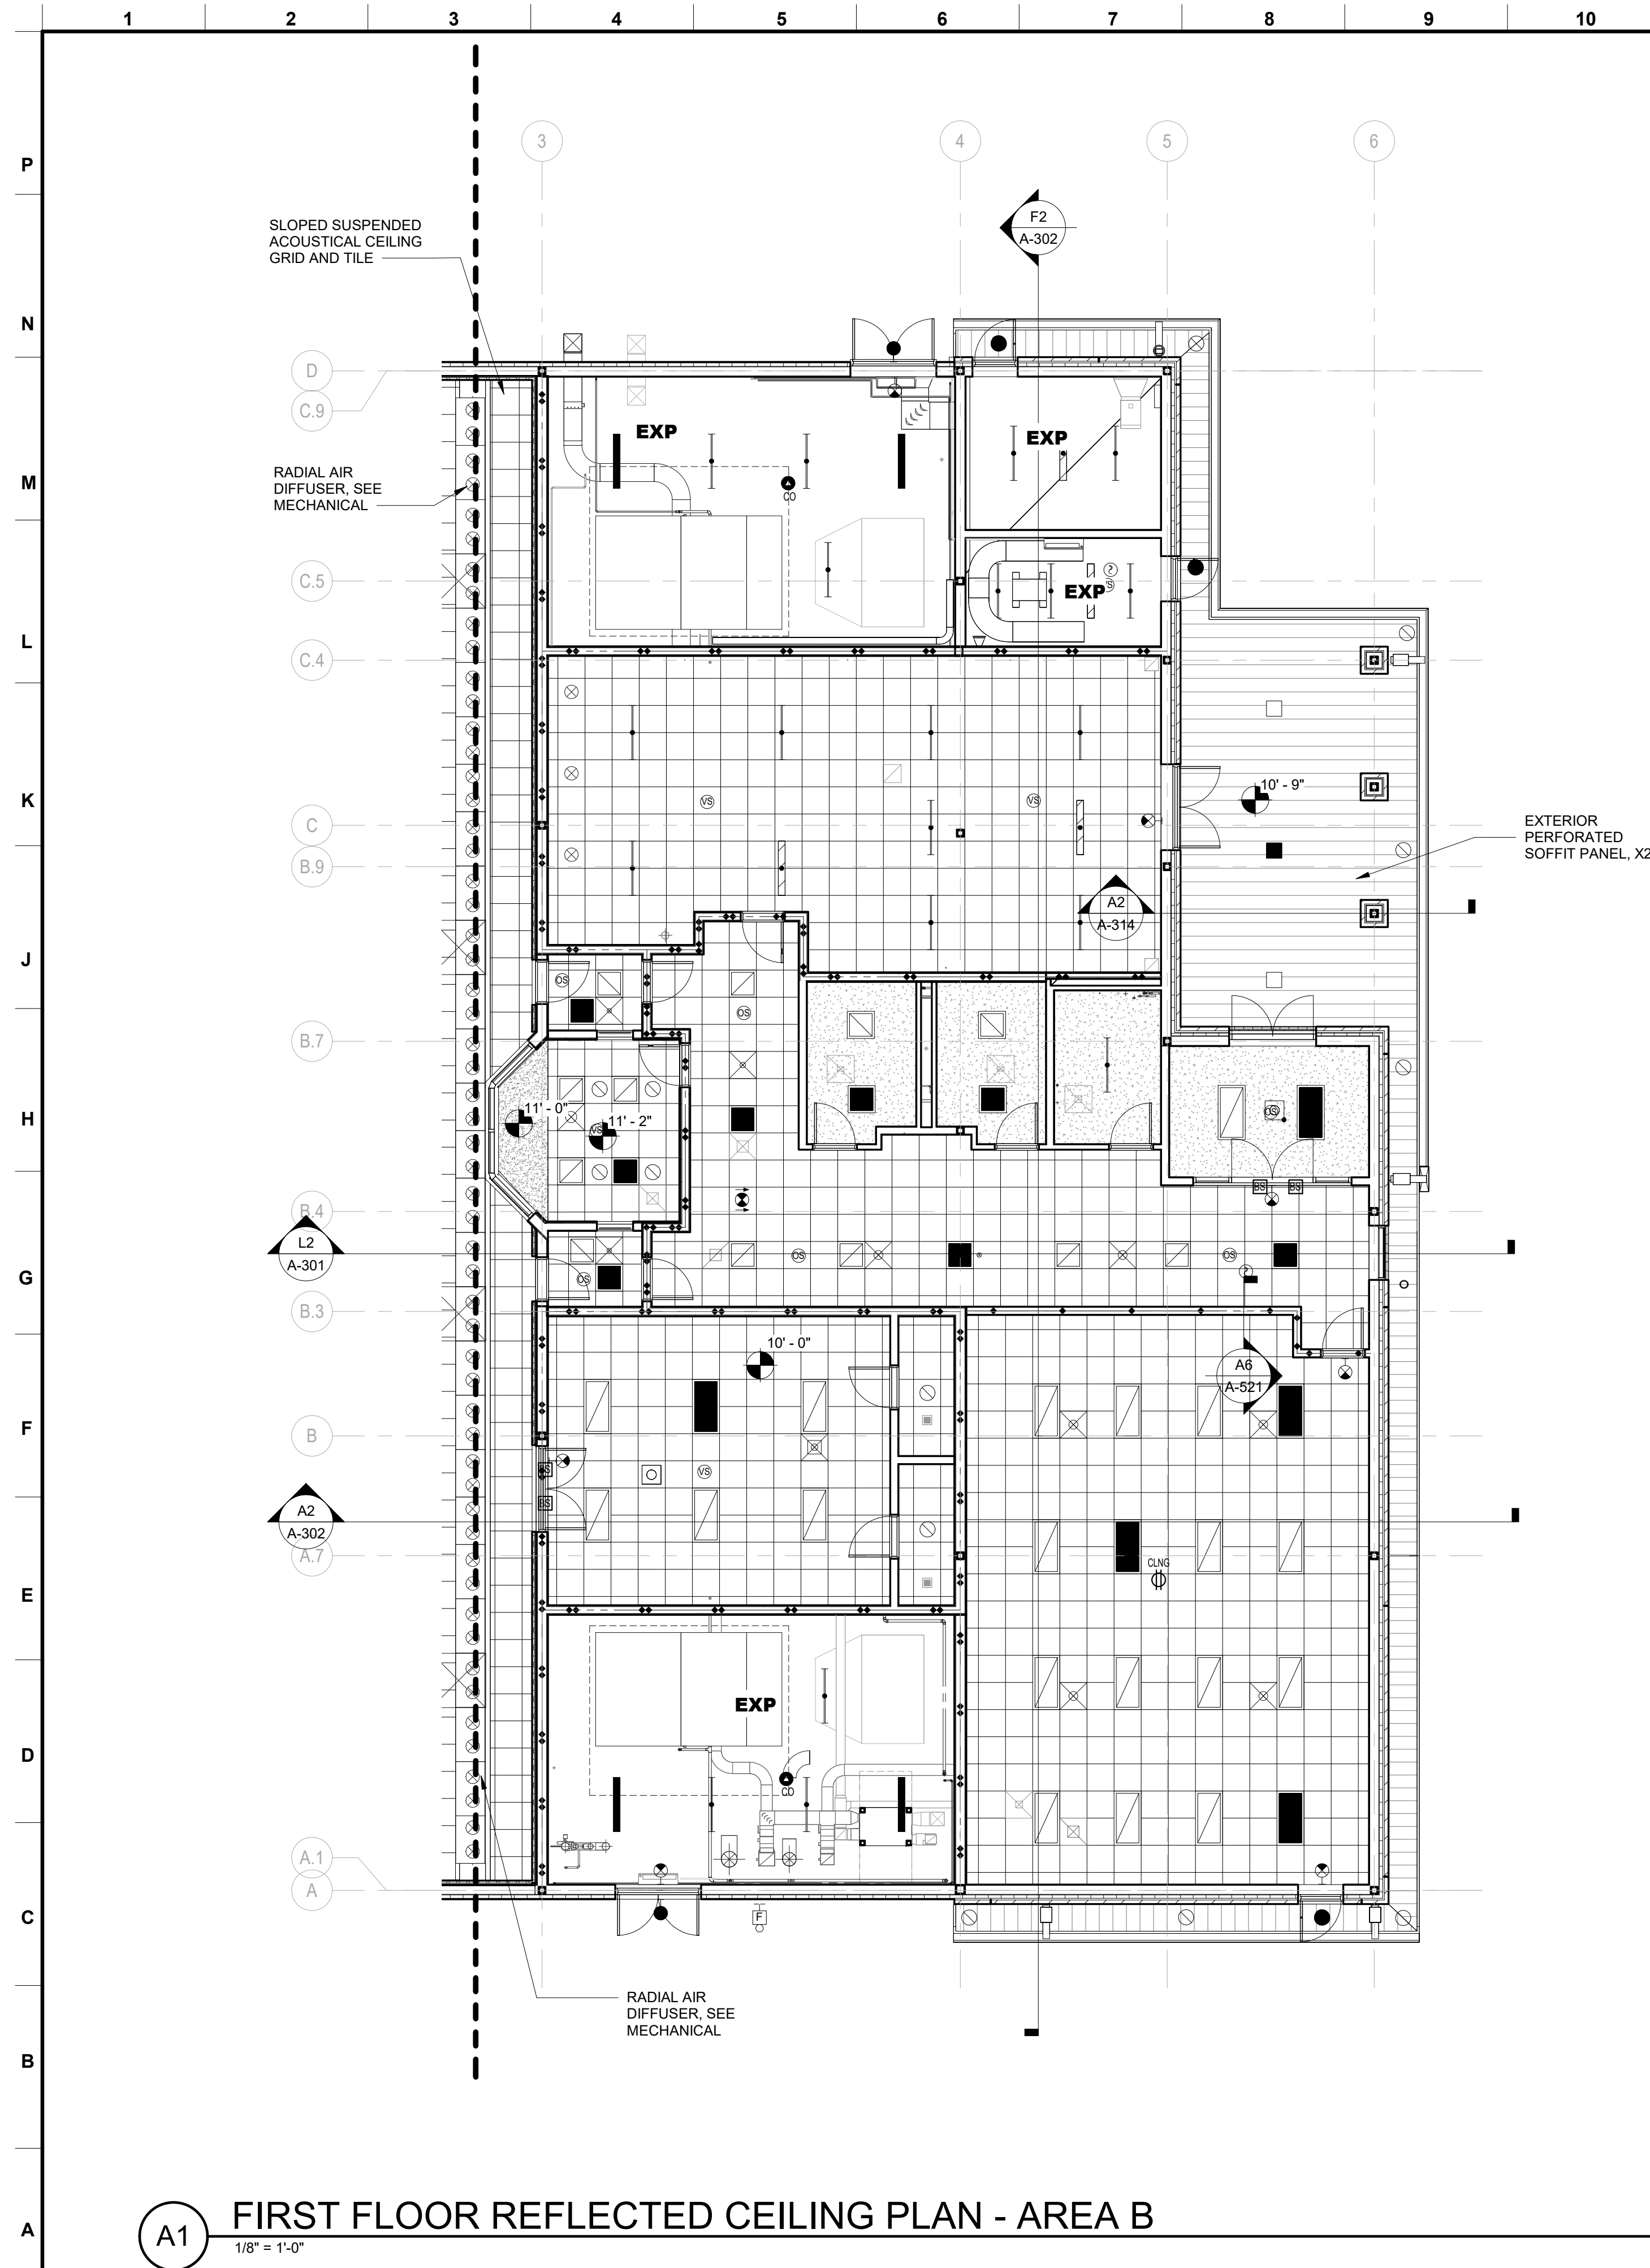

GENERAL NOTES - CEILING

1. ALL CEILINGS SHALL BE AT 9'-0", U.N.O.
2. SUSPENDED ACoustICAL AND GYPSUM BOARD CEILINGS REQUIRE BRACING, REFERENCE SPEC SECTIONS 09 29 00 GYPSUM BOARD AND 09 51 00 ACoustICAL CEILINGS FOR FURTHER INFORMATION.
3. PROVIDE MOISTURE RESISTANT GYPSUM BOARD AT ALL WET LOCATIONS SUCH AS JANITORS CLOSETS, RESTROOMS AND BREAKROOMS.
4. REFERENCE SHEET A-631 FOR BAFFLE AND SAFETY CEILING DETAILS

LEGEND - CEILING

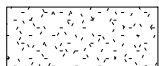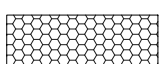	ACOUSTICAL CEILING TILES	 OR  OR 	EMERGENCY LIGHT FIXTURE
	5/8" TYPE "X" GYPSUM WALL BOARD		INDUSTRIAL STRIP LIGHT FIXTURE
	SAFETY CEILING WITH SLAT PROTECTION PER UFC 4-179-02 AND ACOUSTICAL PANEL ON PLYWOOD	 OR 	SUPPLY DIFFUSER
			RETURN GRILLE
			EXHAUST GRILLE
EXP	EXPOSED STRUCTURAL TO BE PAINTED, SEE FINISH SCHEDULE		EXIT SIGN LOCATION
	RECESSED CAN LIGHTING FIXTURE	 OR 	EXTERIOR LIGHT FIXTURES
 OR  OR 	RECTANGULAR LIGHT FIXTURE		



**US Army Corps
of Engineers®**

[illegible]

DESIGNED BY: M. SCHENKENFELDER	ISSUE DATE: SEPTEMBER 2024
DRAWN BY: R. HOE	SOLICITATION NO.:
CHECKED BY: D. BANJANOVIC	CONTRACT NO.:
SUBMITTED BY: J. MACMILLAN	DRAWING CODE:
SIZE: A	
SCALE:	

US ARMY CORPS OF ENGINEERS
LOUISVILLE DISTRICT
600 DR. MARTIN LUTHER KING JR. PLACE
LOUISVILLE KY 40202

GRISSOM AIR RESERVE BASE
INDOOR SMALL ARMS RANGE
PN CTGB129032, P2 502689, FY 25


FIRST FLOOR REFLECTED CEILING PLAN - AREA B

SHEET ID

A-142

CERTIFIED FINAL

W912QR25B0001 Plans-0000

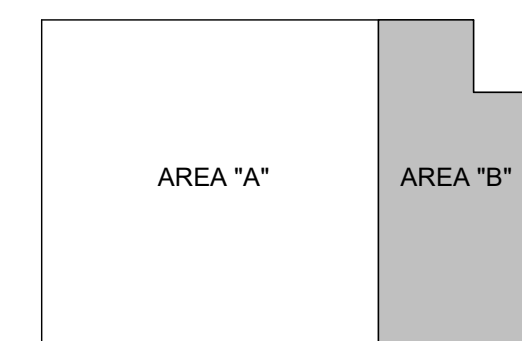

PLAN NORTH

